



CONCEPT, NOT FOR FABRICATION


REV	DESCRIPTION	DATE	BY
P1	Concept sheet	2026-09-25	AC

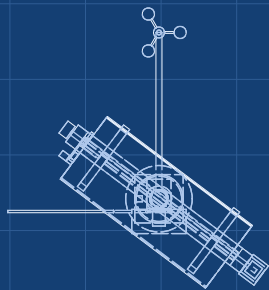



TOP VIEW
Scale 1:25

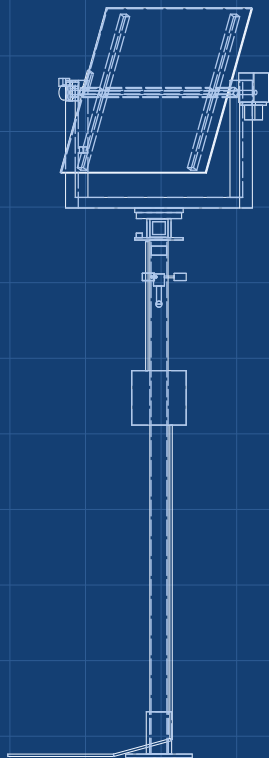

FRONT VIEW
Scale 1:25

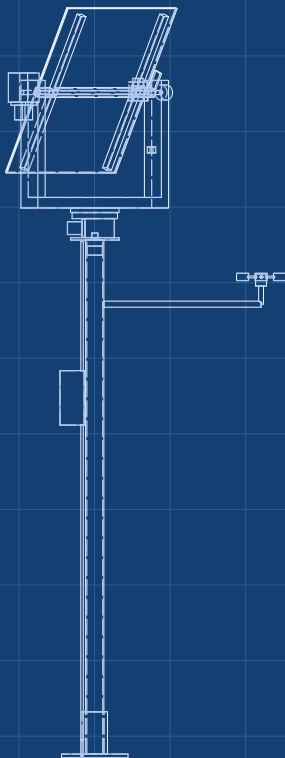

RIGHT VIEW
Scale 1:25

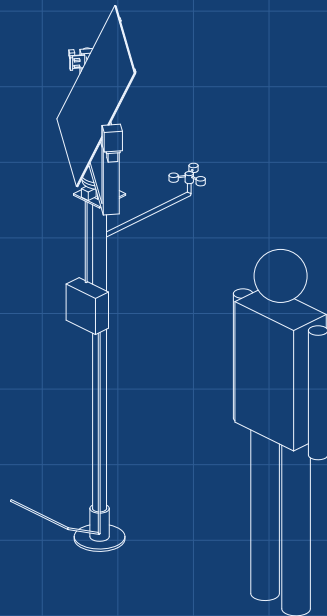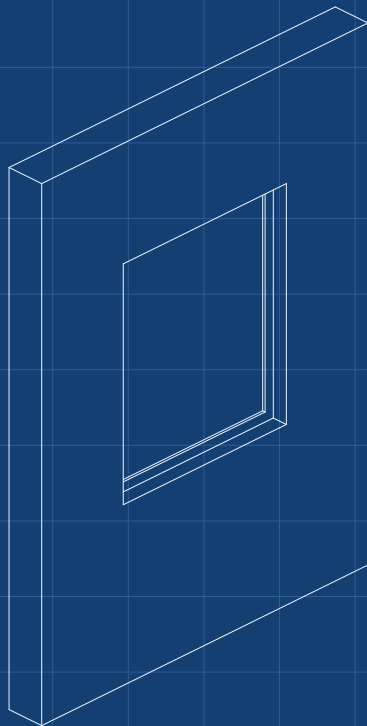

ISOMETRIC VIEW
Not to scale; figure is a 1.75 m person

KEY FIGURES

Mirror 600 x 600 mm (0.36 m²), center 2.2 m above ground
About 159 W of sunlight into the room at 800 W/m² DNI [A2]
0.5 kWh (21 Dec) to 1.0 kWh (1 Feb) into the room, reference site [B3]
Open loop: sun-position algorithm and RTC, no sun sensor
Beam error 0.31° typical against 0.5° with preload springs [D5]
Face-down stow in 23 s; latch carries the storm load [F1, E7]
Parts \$451 against \$430 budget, R15 not met [J1]

HELIOLITE

Two-axis mini heliostat concept

DRAWING NO. HLT-DWG-010			REV P1	SHEET 1 of 1	SIZE ANSI B
SCALE 1:25	UNITS mm	PROJECTION 	DATE 2026-09-25	DRAWN Amish Chadha	

MATERIAL / NOTES
Massing model for concept communication