



CONCEPT, NOT FOR FABRICATION


REV	DESCRIPTION	DATE	BY
P1	Concept sheet	2026-09-25	AC

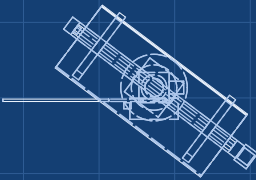


TOP VIEW
Scale 1:25

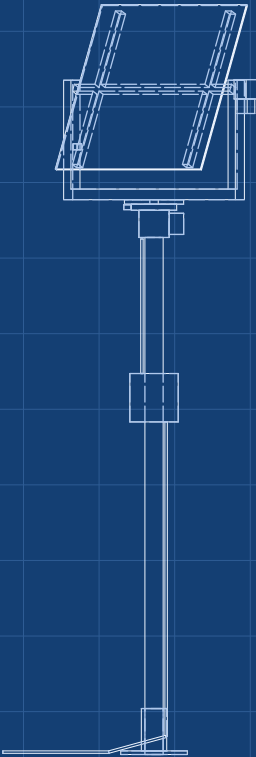

FRONT VIEW
Scale 1:25

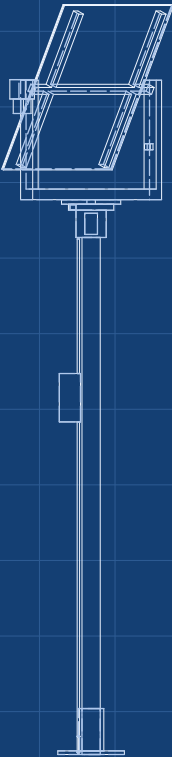

RIGHT VIEW
Scale 1:25

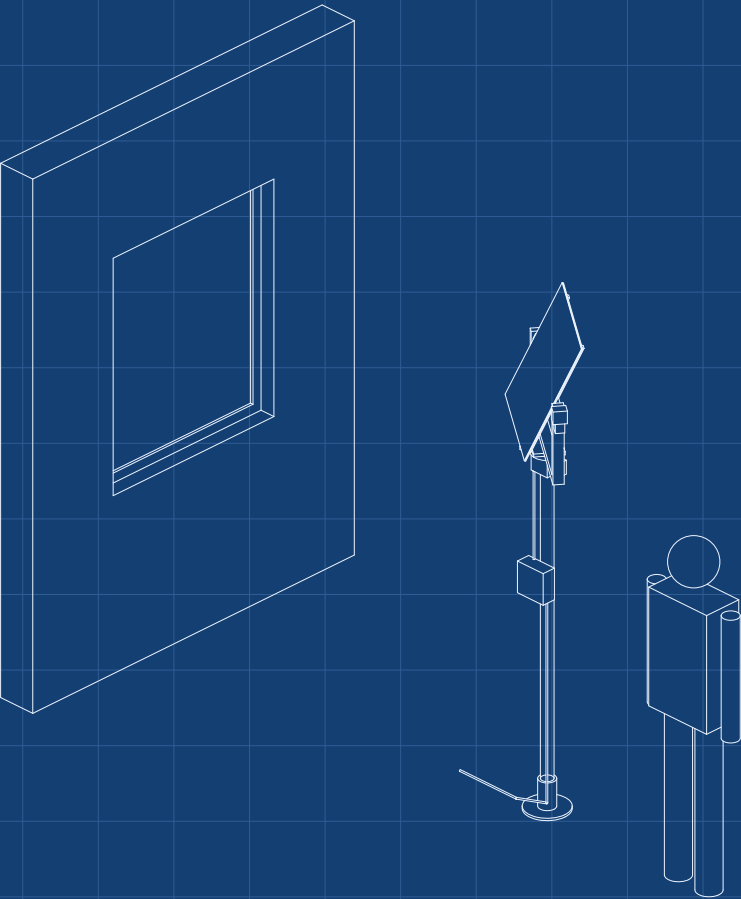

ISOMETRIC VIEW
Not to scale; figure is a 1.75 m person

KEY FIGURES

Mirror 600 x 600 mm (0.36 m²), center 2.2 m above ground
About 160 W of sunlight into the room at 800 W/m² DNI (estimate)
About 0.7 kWh through the glazing on a clear winter day (estimate)
Open loop: sun-position algorithm and RTC, no sun sensor
Beam pointing target 0.5° (about 90 mm at 10 m); face-down stow
Parts about \$390 against \$400 budget (indicative)

HELIOLITE

Two-axis mini heliostat concept

DRAWING NO.

HLT-DWG-010

REV

P1

SHEET

1 of 1

SIZE

ANSI B

SCALE

1:25

UNITS

mm

PROJECTION



DATE

2026-09-25

DRAWN

Amish Chadha

MATERIAL / NOTES

Massing model for concept communication